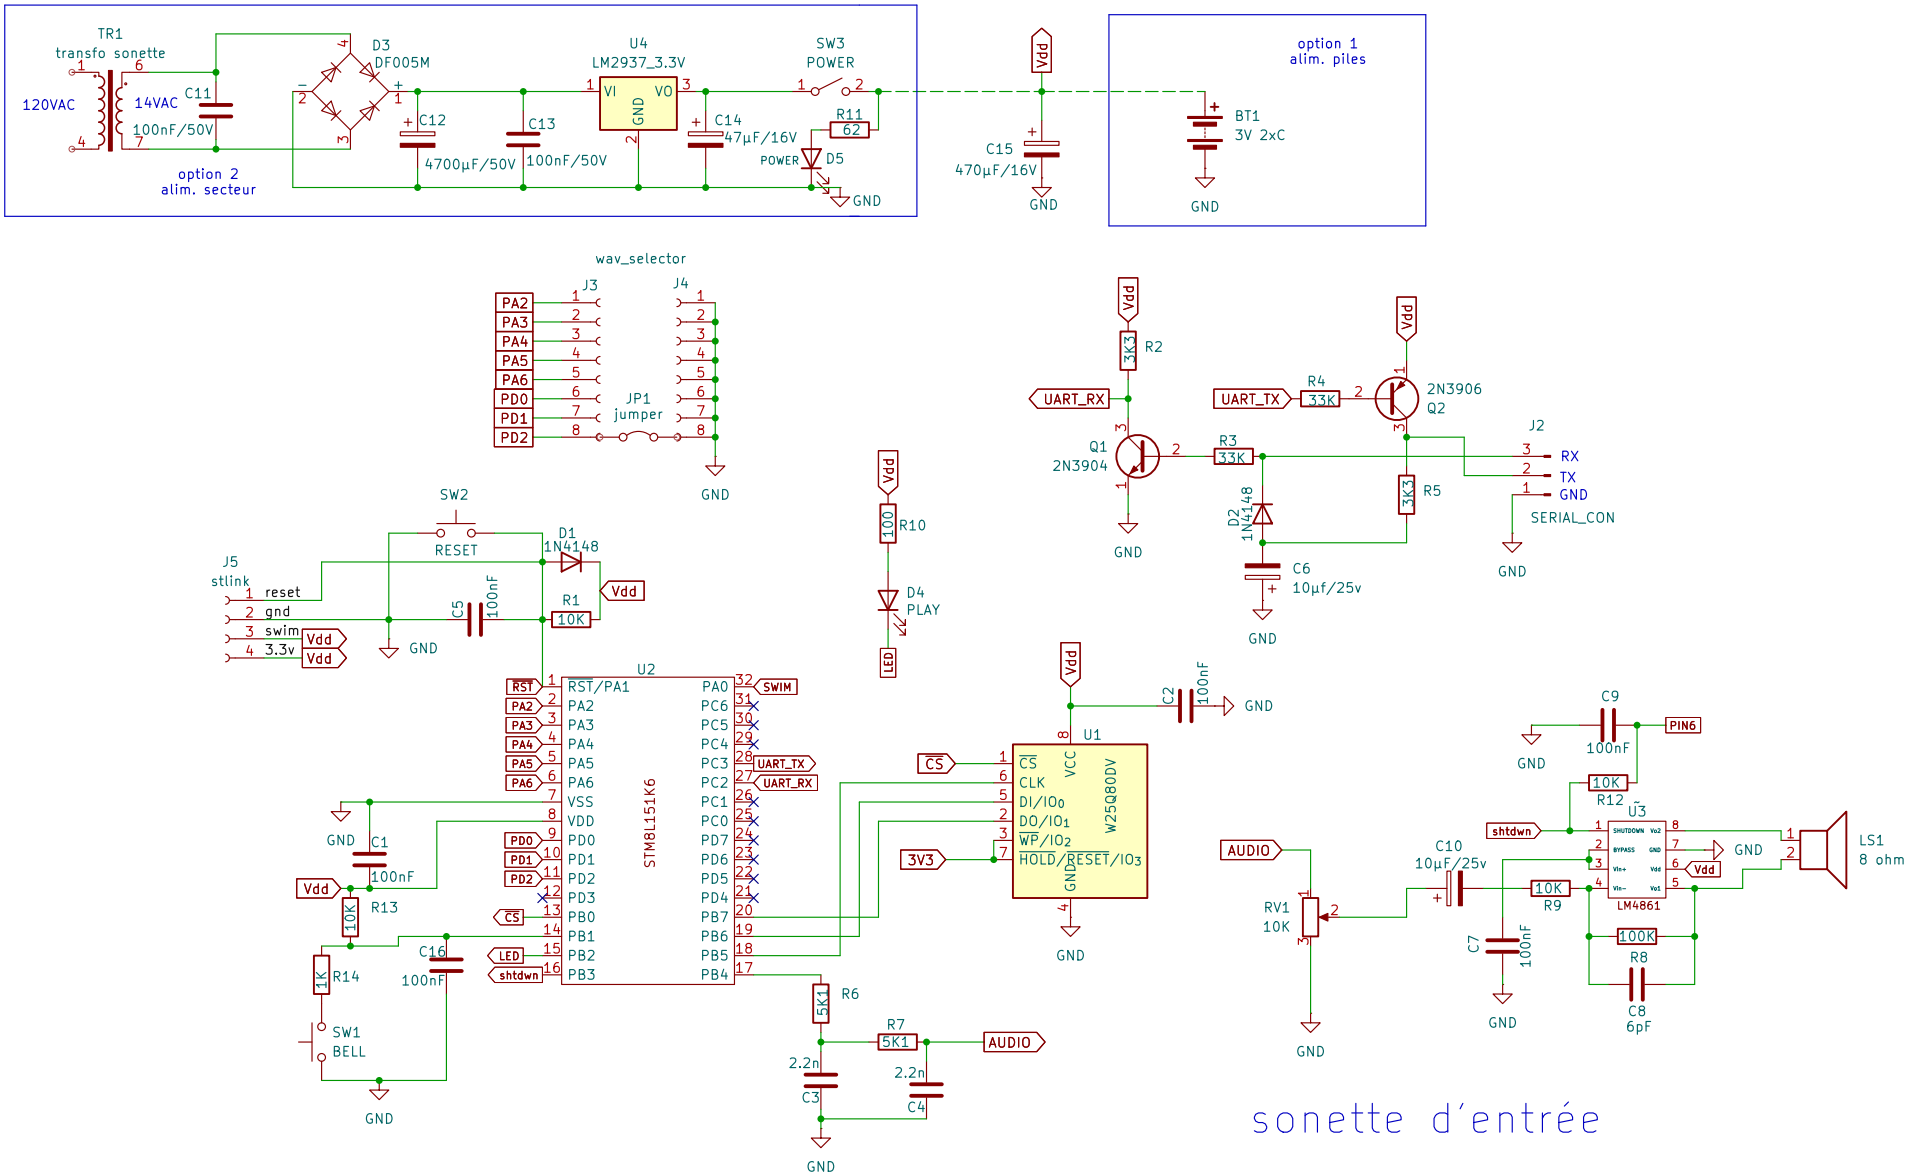



sonette d'entrée